




Кабель-канал 80х60
Заглушка 80х60
1м
Плоский угол 80х60
Рамка 80х80
Вставка 45х45
Модуля RJ45


Кабель-канал 80х60
Заглушка 80х60
1м
1м
Заглушка 80х60
Рамка 80х80
Вставка 45х45
Модуля RJ45
Тройник/отвод 80х60
Рамка 80х80
Вставка 45х45
Модуля RJ45

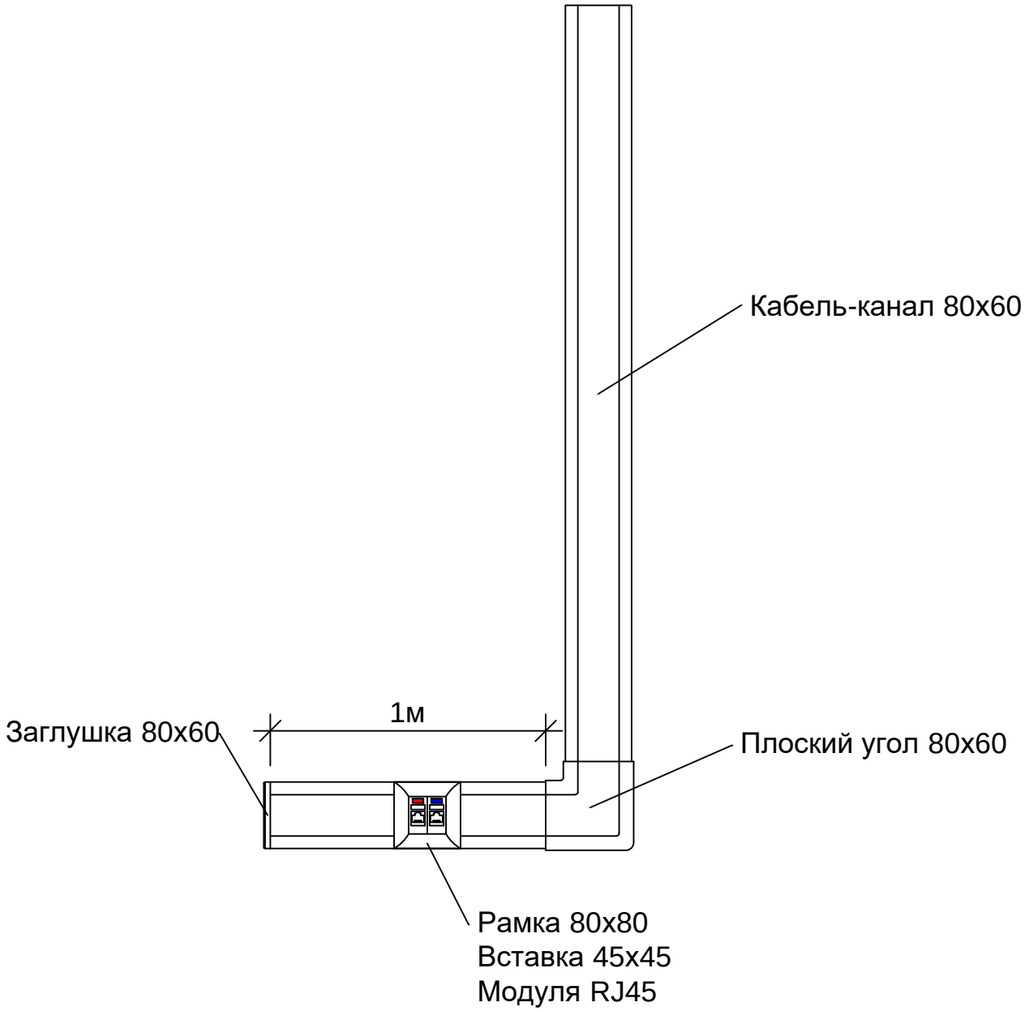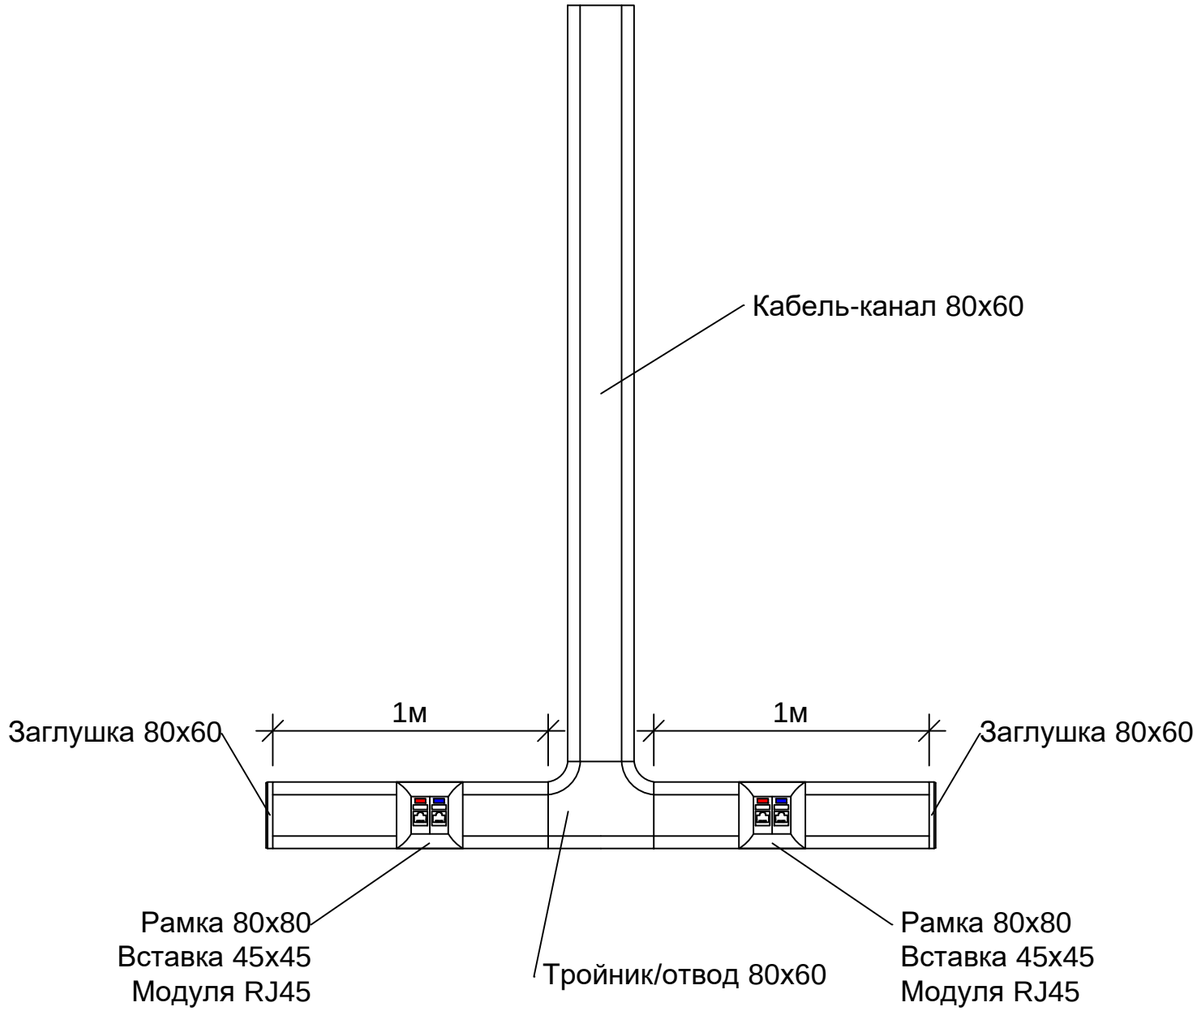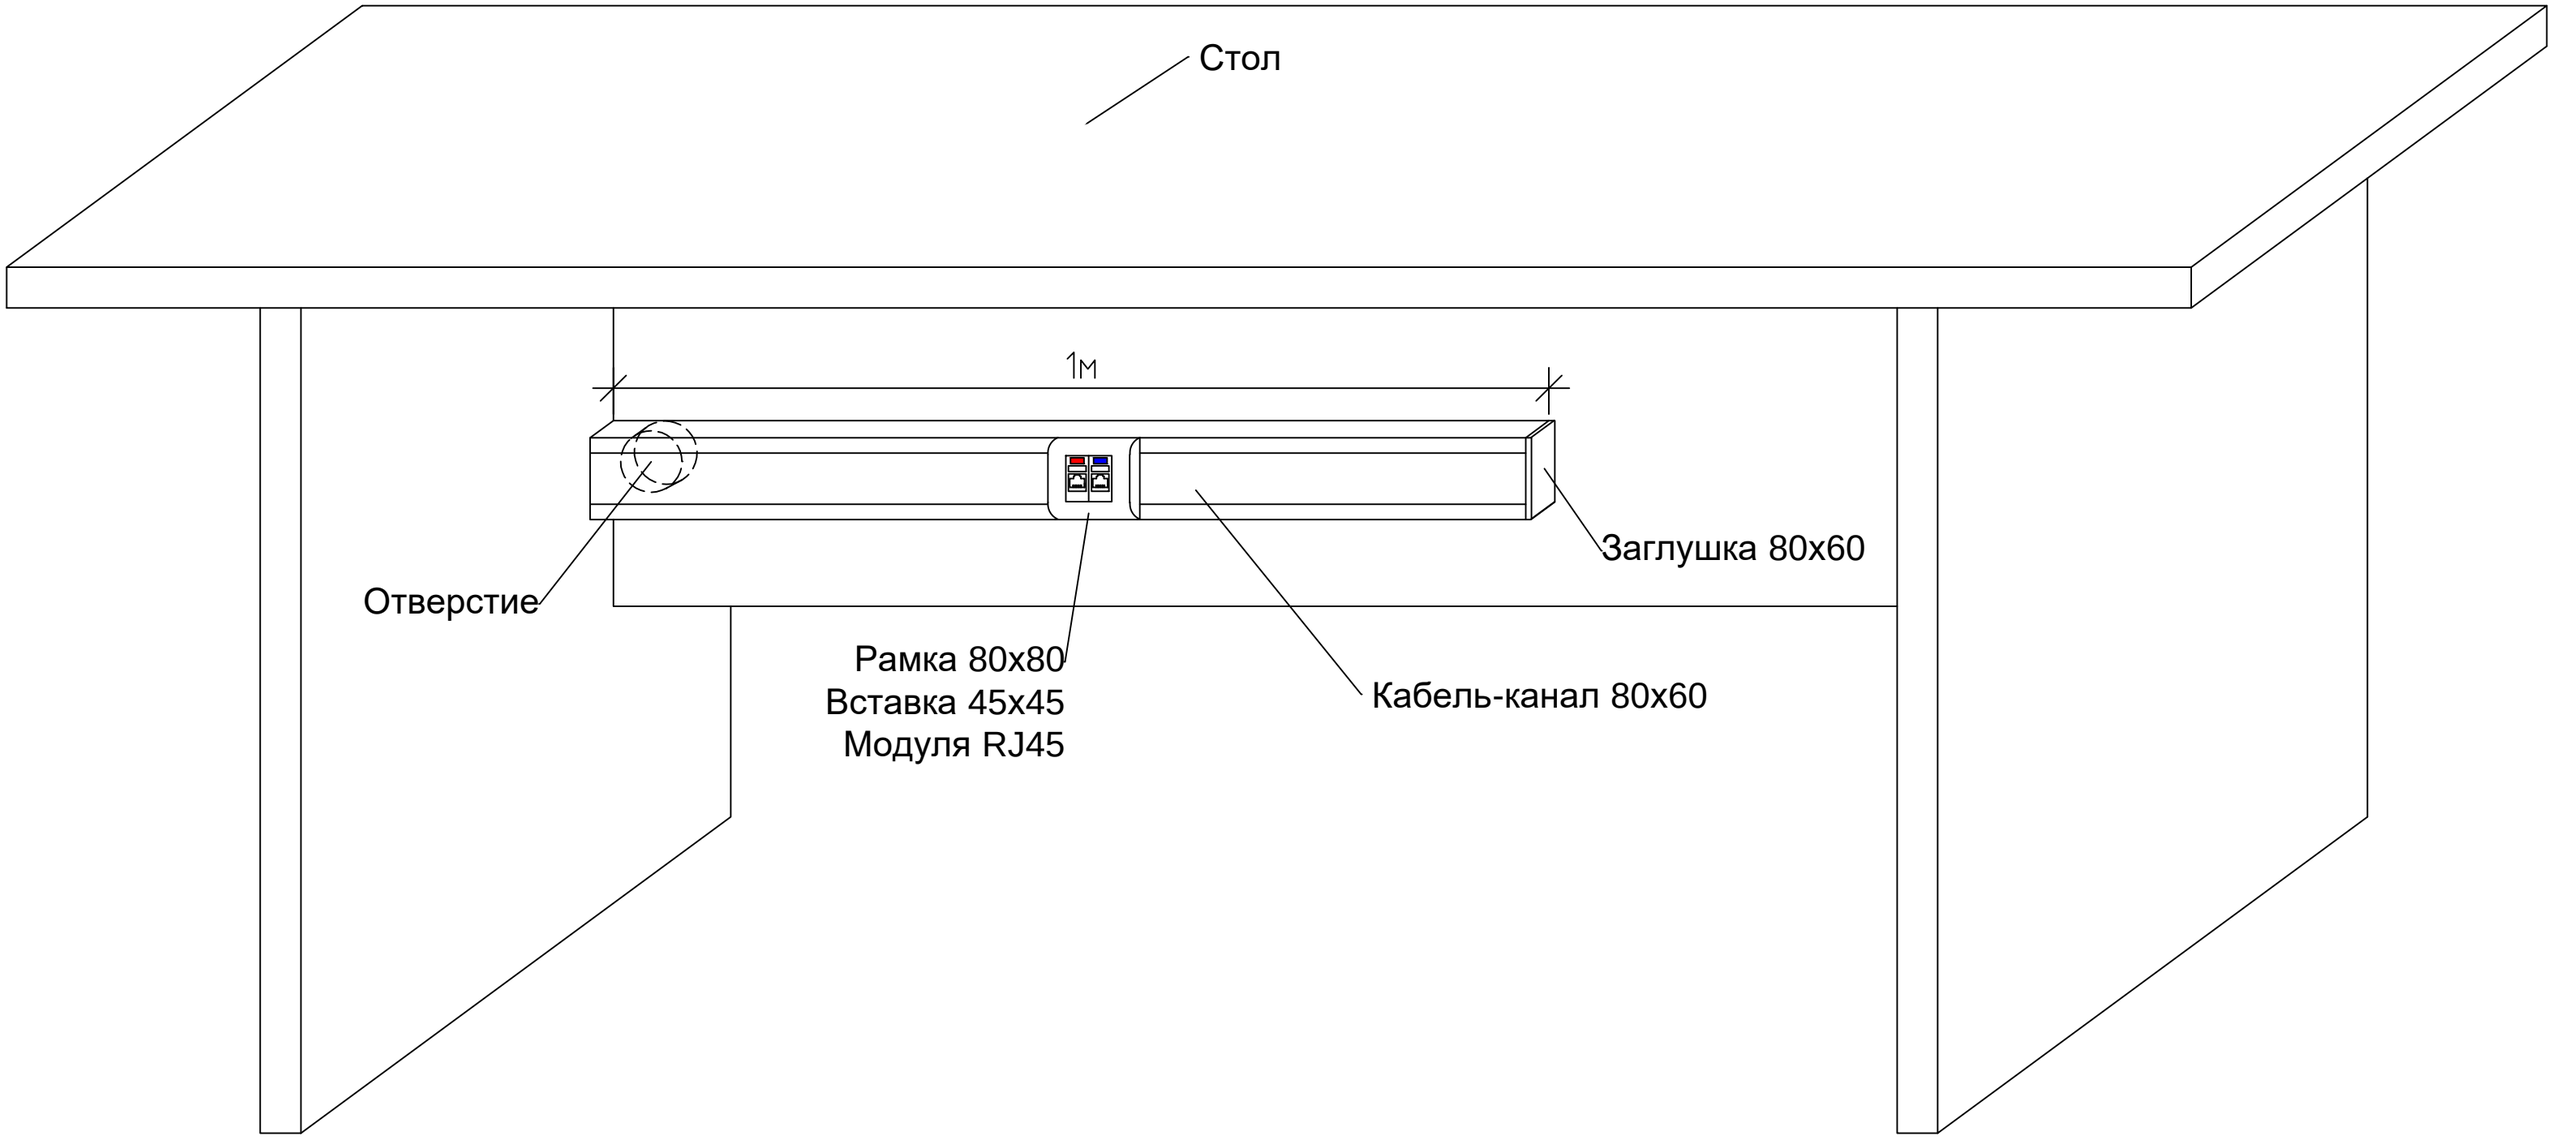



Если длина стола менее 1 метра,
то кабель-канал делаем на всю его длину

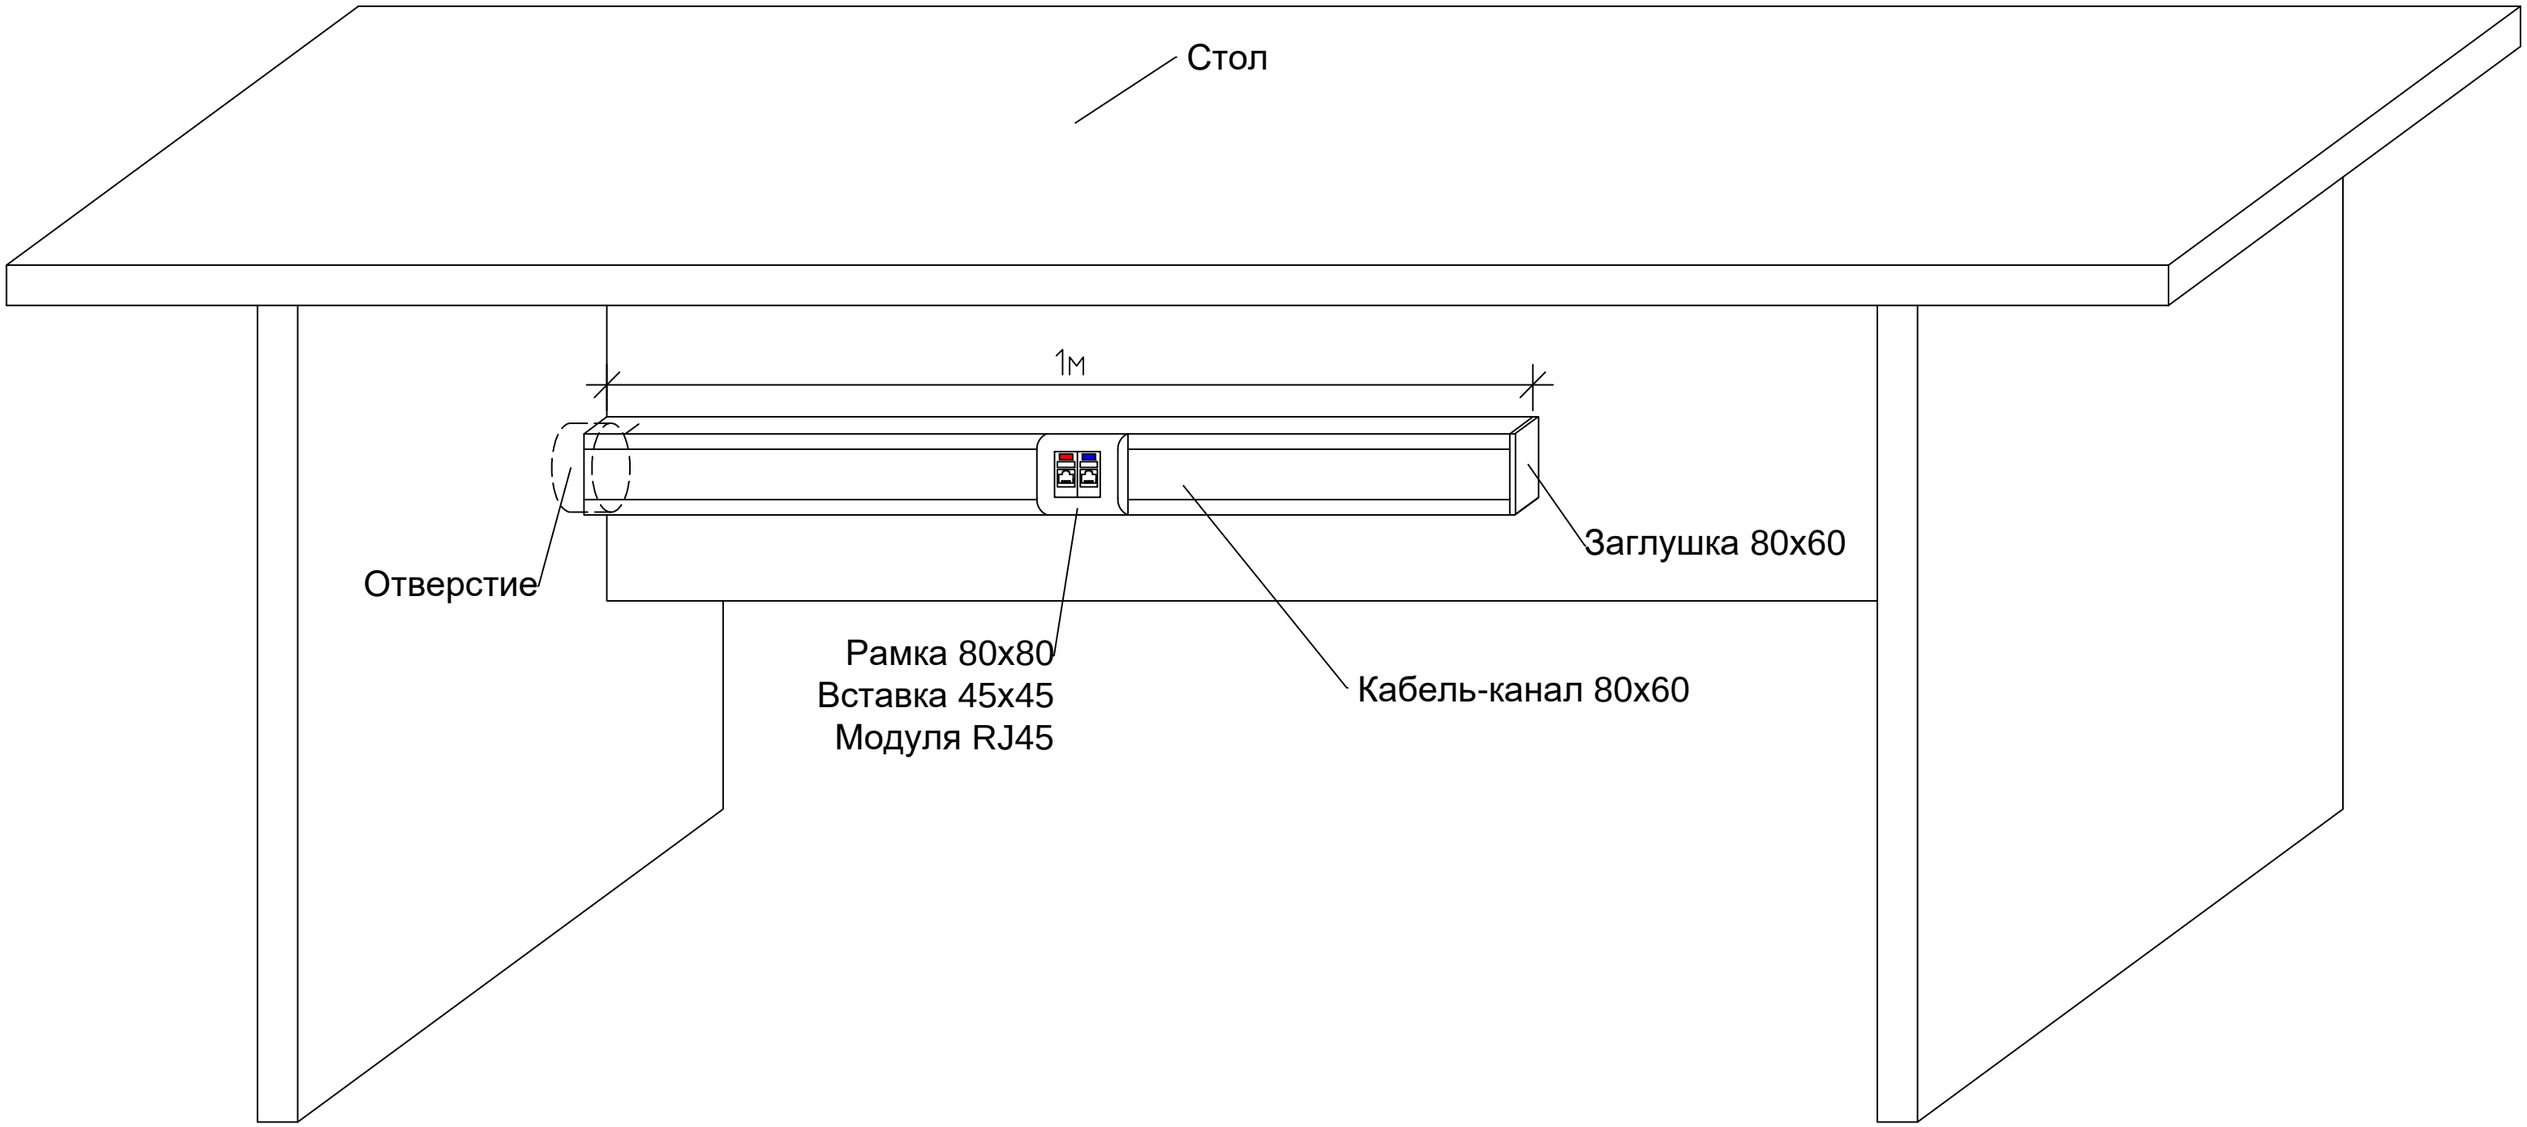

Если длина стола менее 1 метра,
то кабель-канал делаем на всю его длину

Выпуск металлорукава должен быть 1,5 метра.
Выпуск кабеля UTP должен быть 0,5 метра

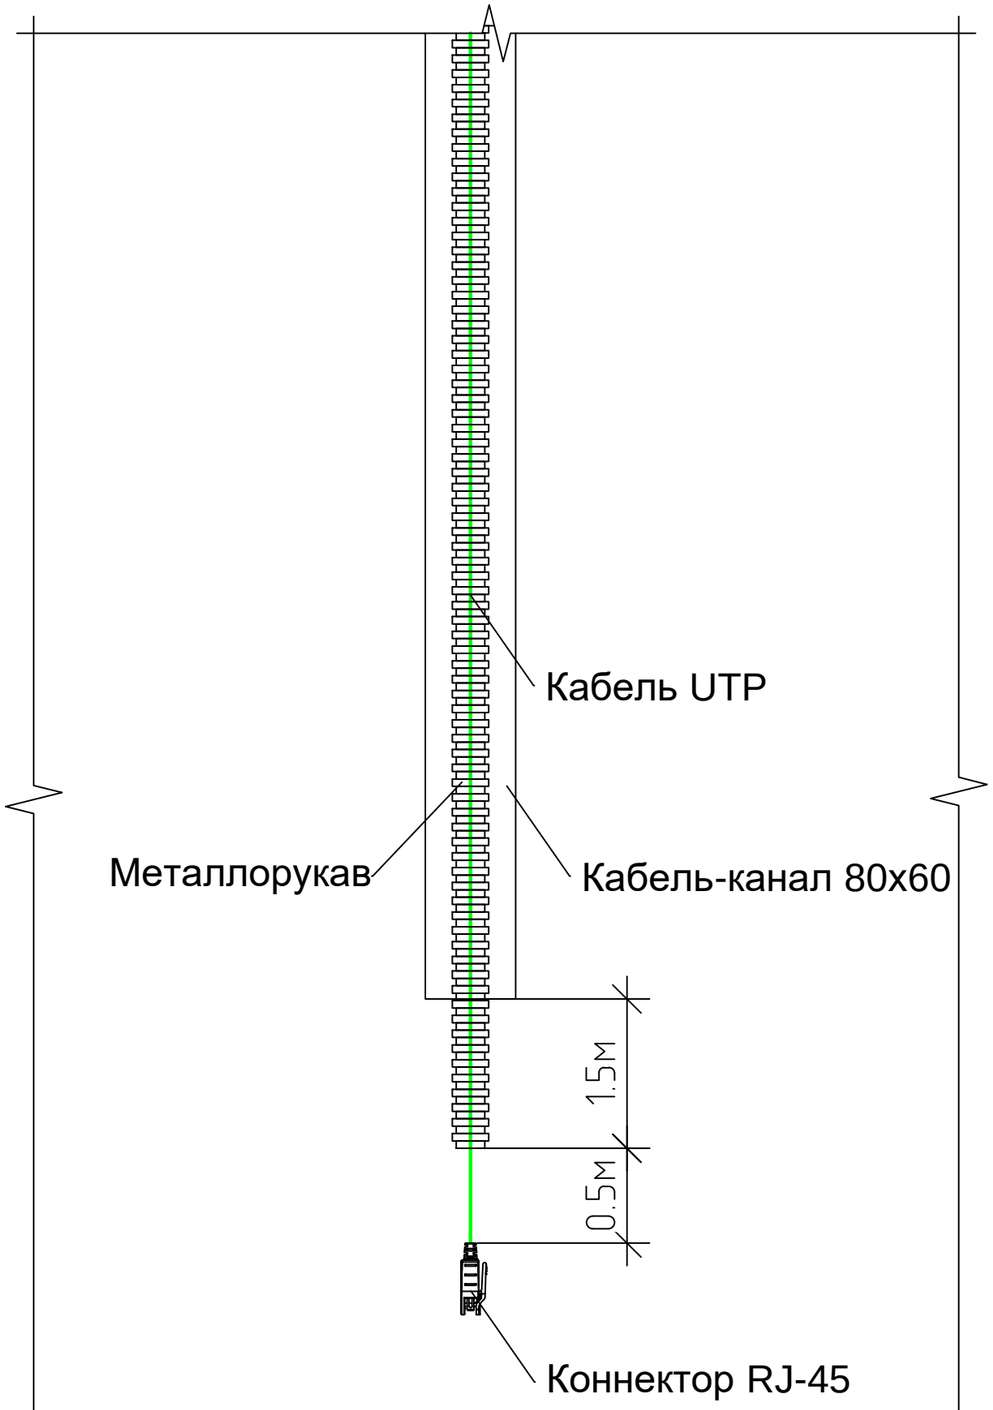

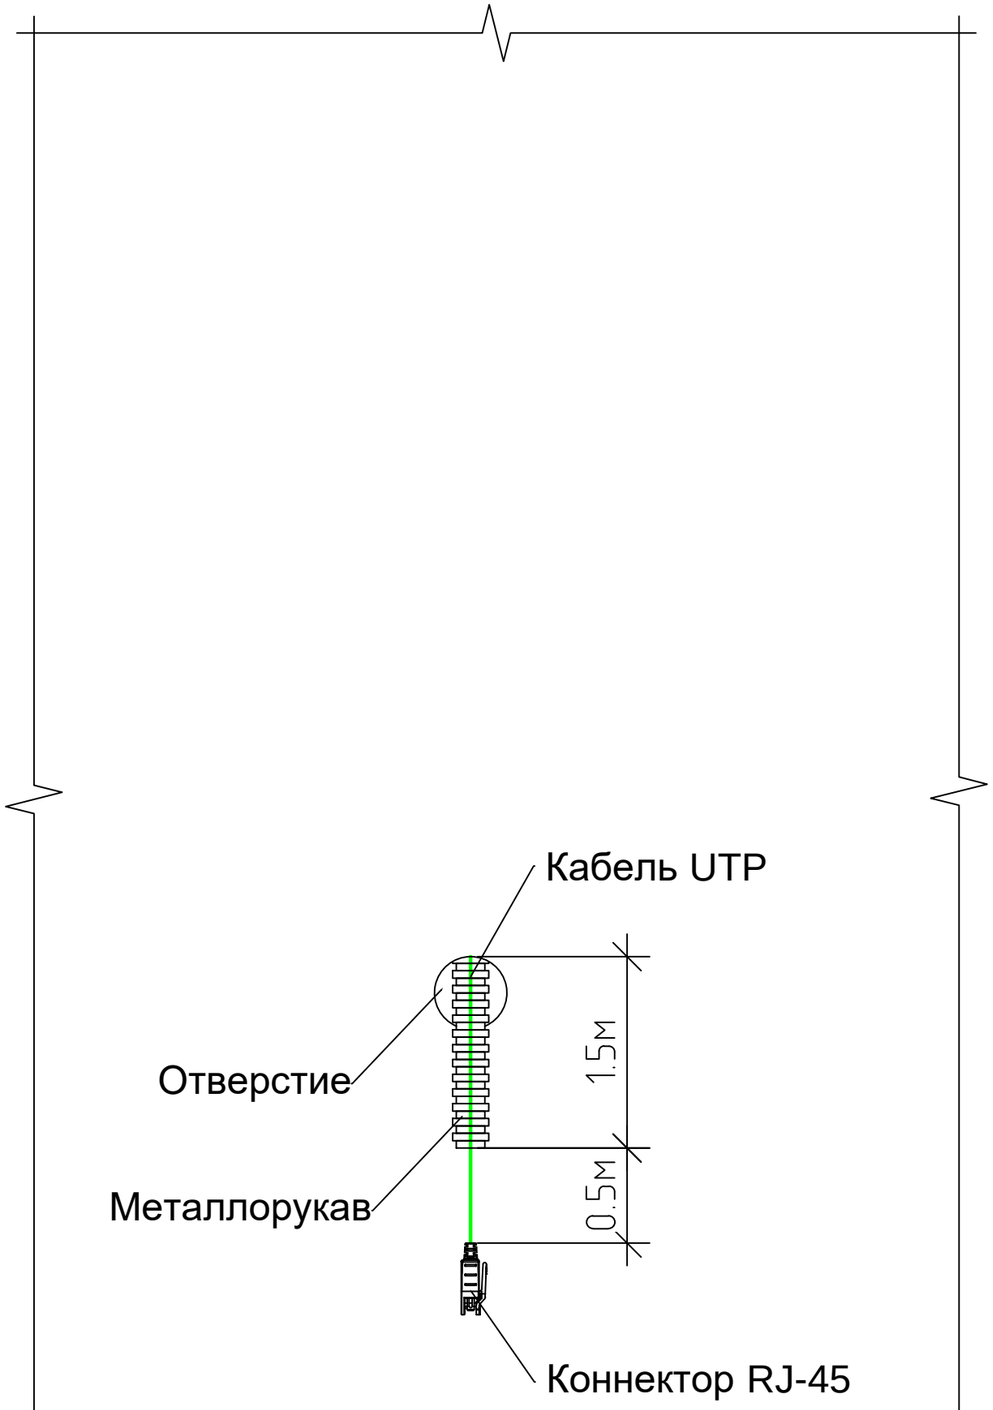


До точки спуска кабель прокладывается в гофрированной трубе за потолком



До точки спуска кабель прокладывается в гофрированной трубе за потолком




До точки спуска кабель прокладывается в гофрированной трубе за потолком.
За стеной кабель прокладывается без гофрированной трубы.

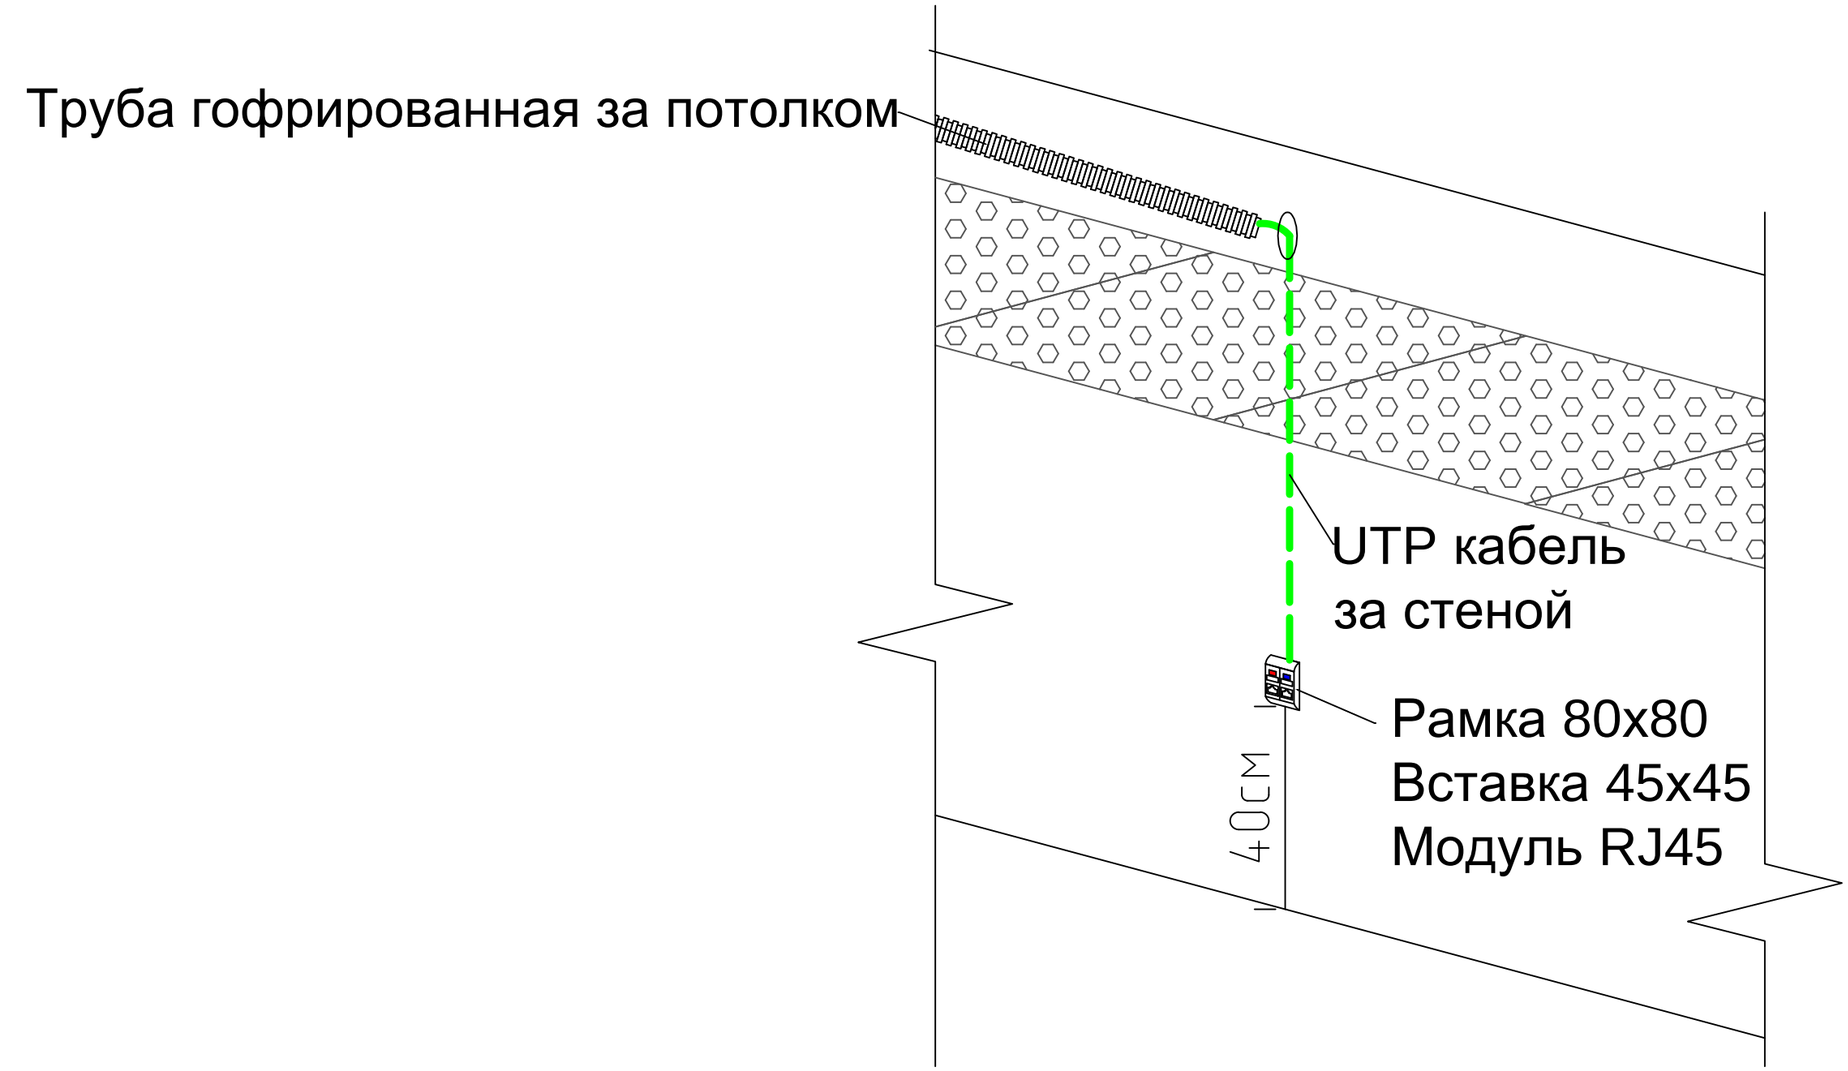





Маркировка выполняется в печатном виде должна быть ровной и последовательной

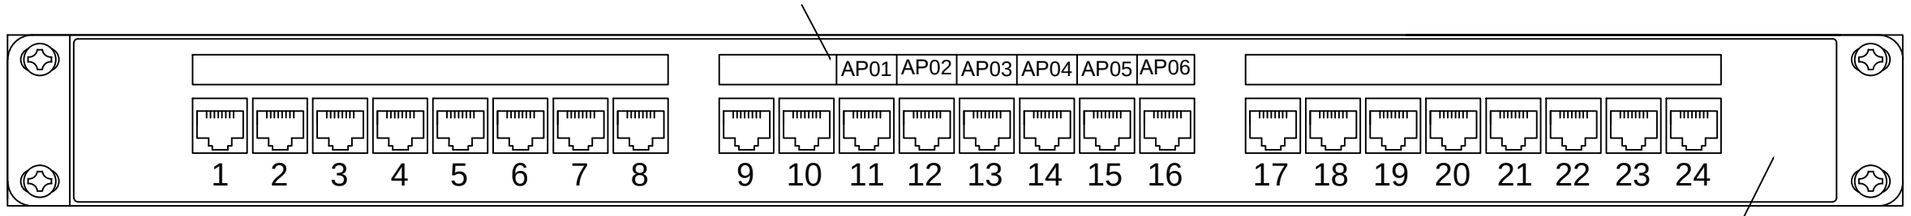

Патч-панель



